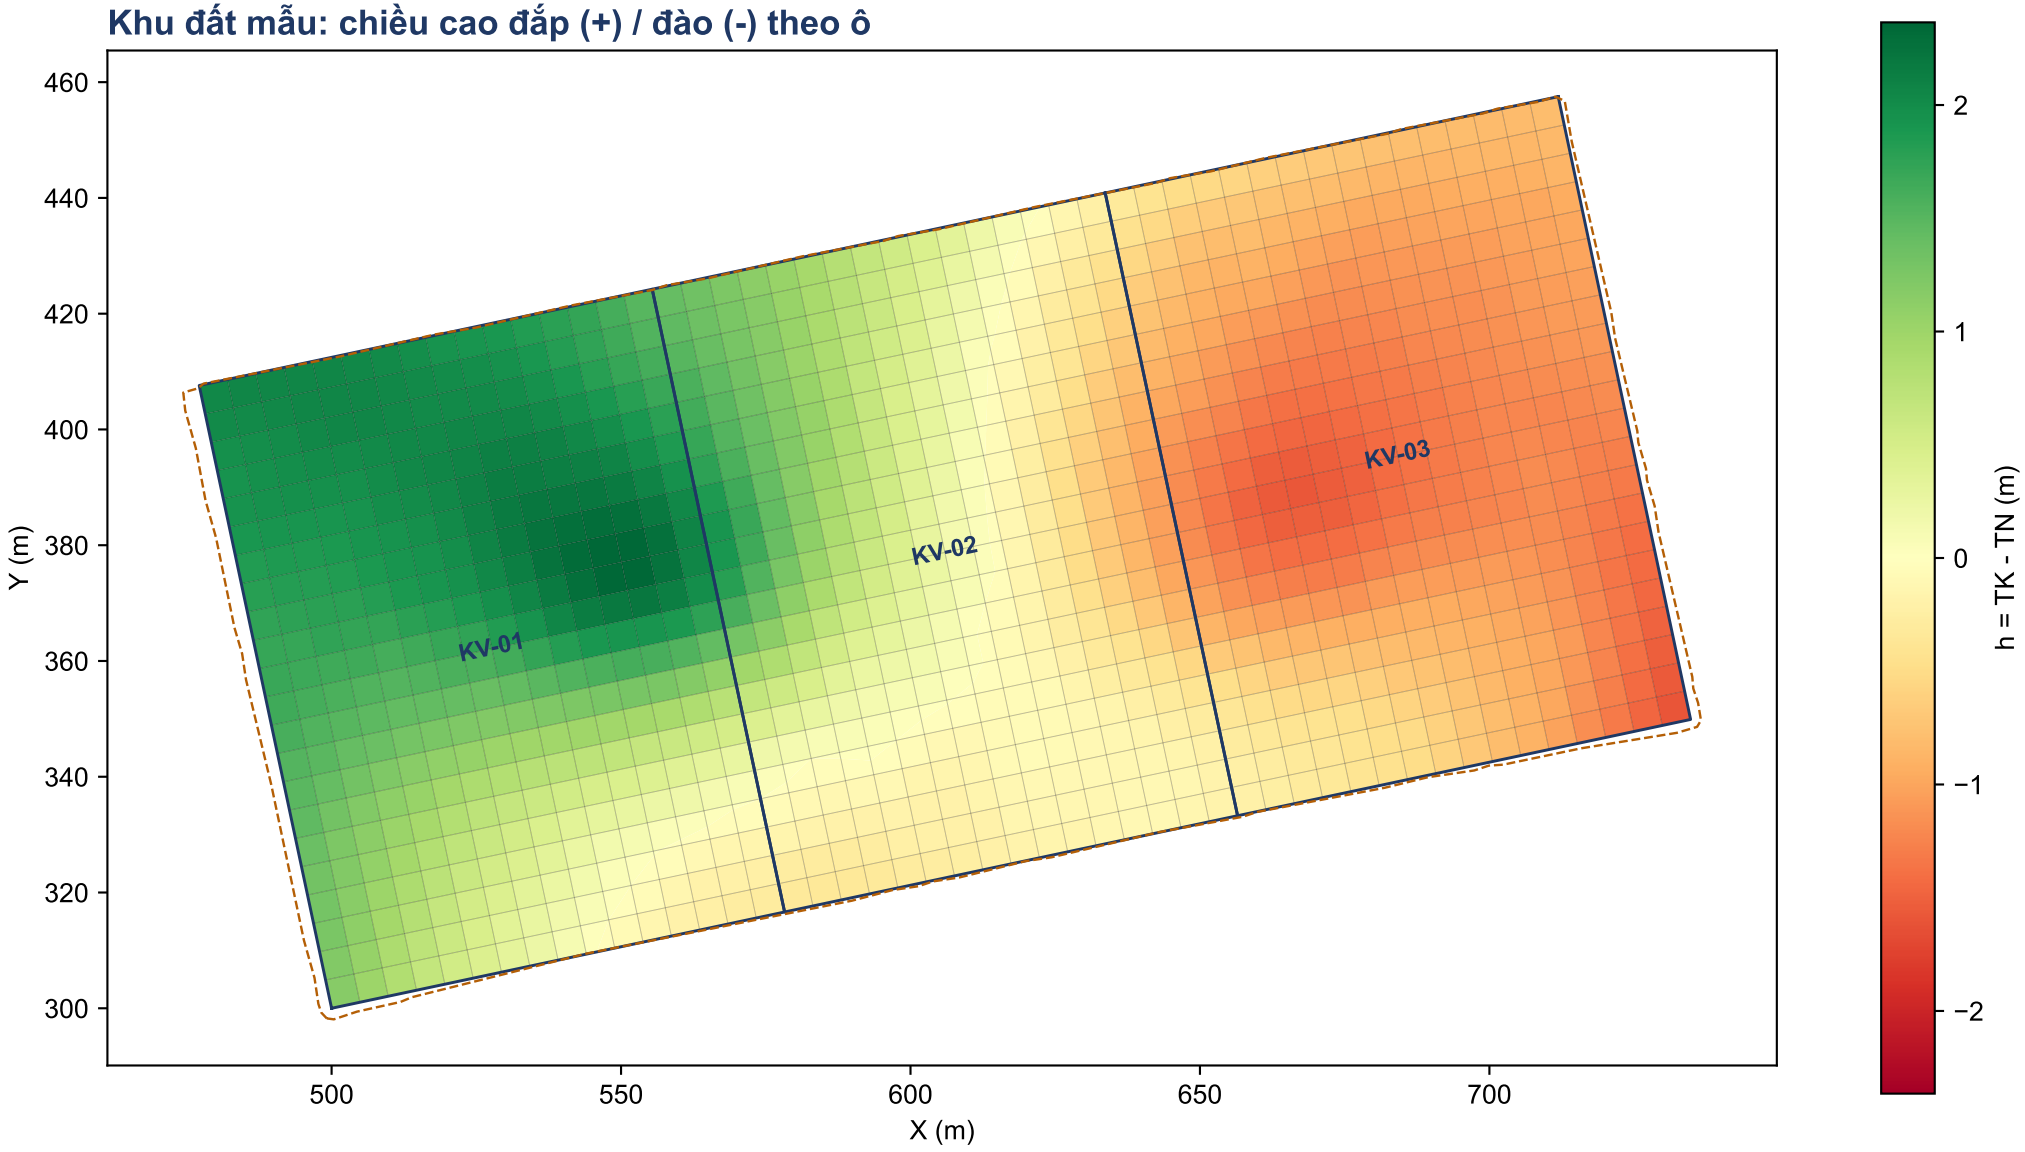
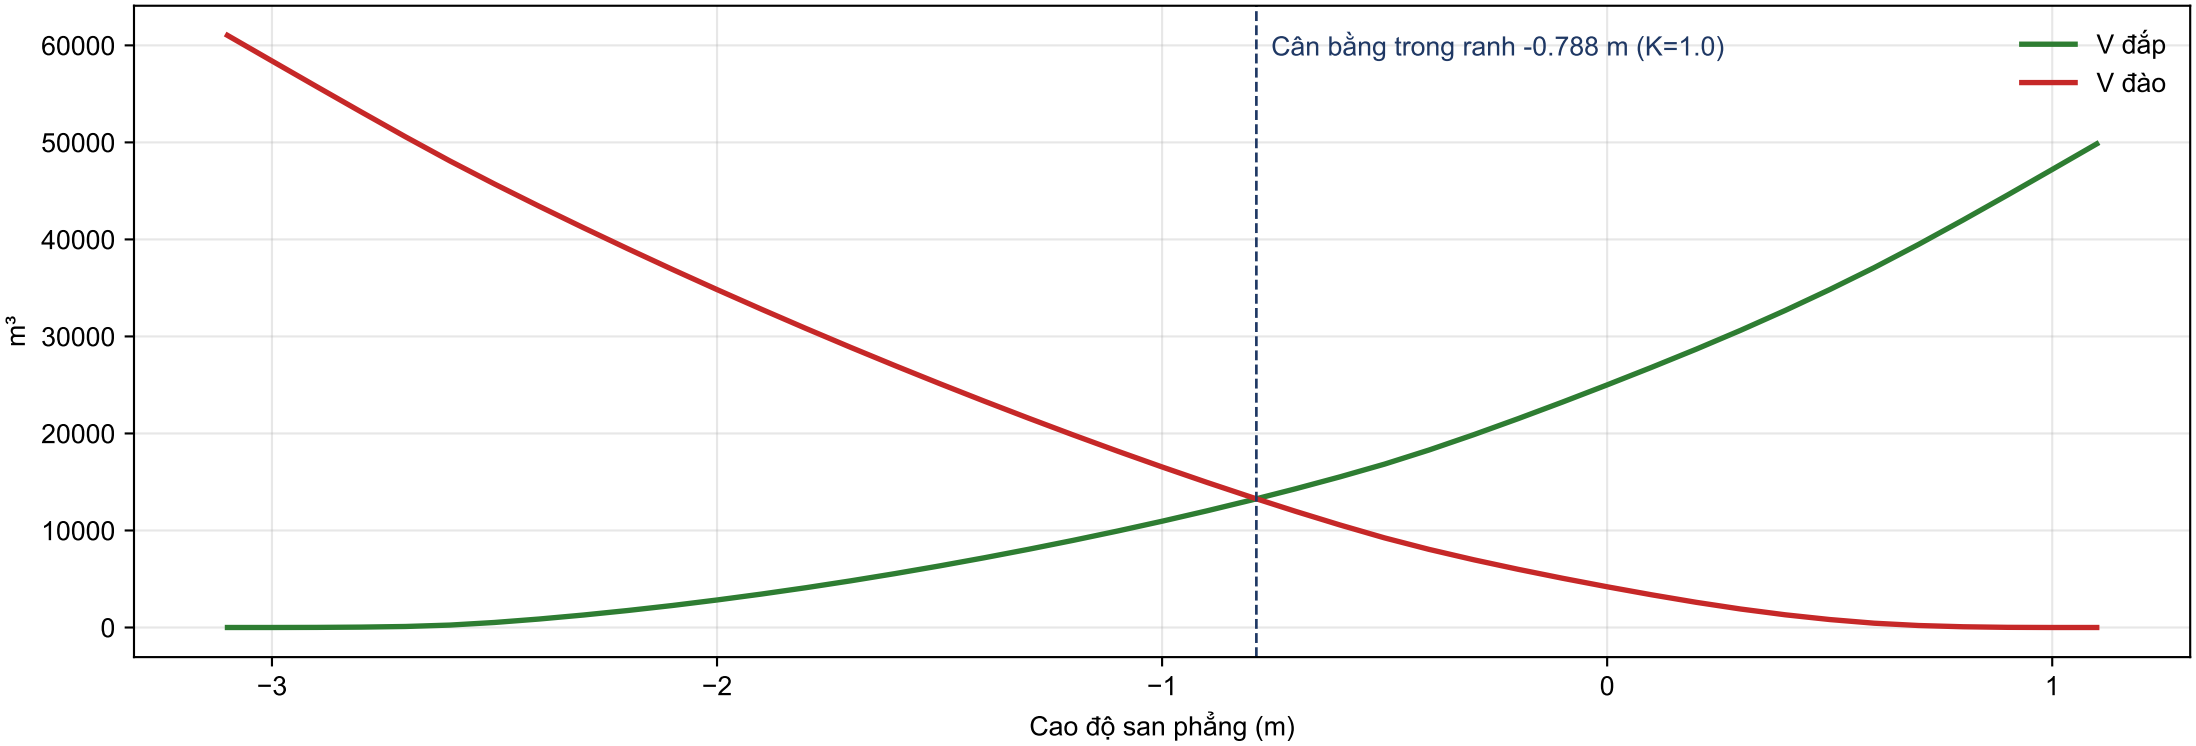

Khu đất mẫu: chiều cao đắp (+) / đào (-) theo ô
KV-01
KV-02
KV-03
Y (m)
X (m)
460
440
420
400
380
360
340
320
300
500
550
600
650
700
h = TK - TN (m)
2
1
0
−1
−2

## Tổng hợp khối lượng (m³)

| Khu vực | Cao độ TK | Diện tích (m²) | V đắp ô | V đào ô | V đắp TIN | V đào TIN |
|---|---|---|---|---|---|---|
| KV-01 | -0.600 | 8,800.0 | 12,411.6 | 64.7 | 12,419.9 | 66.7 |
| KV-02 | -0.600 | 8,800.0 | 3,110.3 | 1,327.1 | 3,111.5 | 1,331.8 |
| KV-03 | -0.600 | 8,800.0 | 0.0 | 9,159.1 | 0.0 | 9,165.1 |
| Taluy | | 538.0 | 246.0 | 123.2 | 246.0 | 123.2 |
| Hố móng | | | 0.0 | 2,412.7 | 0.0 | 2,412.7 |
| Cọc | | | 0.0 | 201.1 | 0.0 | 201.1 |
| **TỔNG** | | **26,938.0** | **15,767.9** | **13,287.8** | **15,777.4** | **13,300.5** |



## Các điểm cần kiểm tra

[CẢNH BÁO] KV-01: 25 ô có tâm cách điểm đo gần nhất trên 7.5 m: A-7, A-13, C-2, C-3, D-2, D-3, D-14, D-15, D-19, E-19, E-20, I-22
[CẢNH BÁO] KV-02: 19 ô có tâm cách điểm đo gần nhất trên 7.5 m: A-7, B-4, E-7, F-8, H-1, H-14, H-15, H-16, I-1, I-7, J-7, K-2
[CẢNH BÁO] KV-03: 22 ô có tâm cách điểm đo gần nhất trên 7.5 m: A-7, B-7, C-2, C-7, C-8, C-9, C-22, J-8, K-8, K-14, K-15, K-20