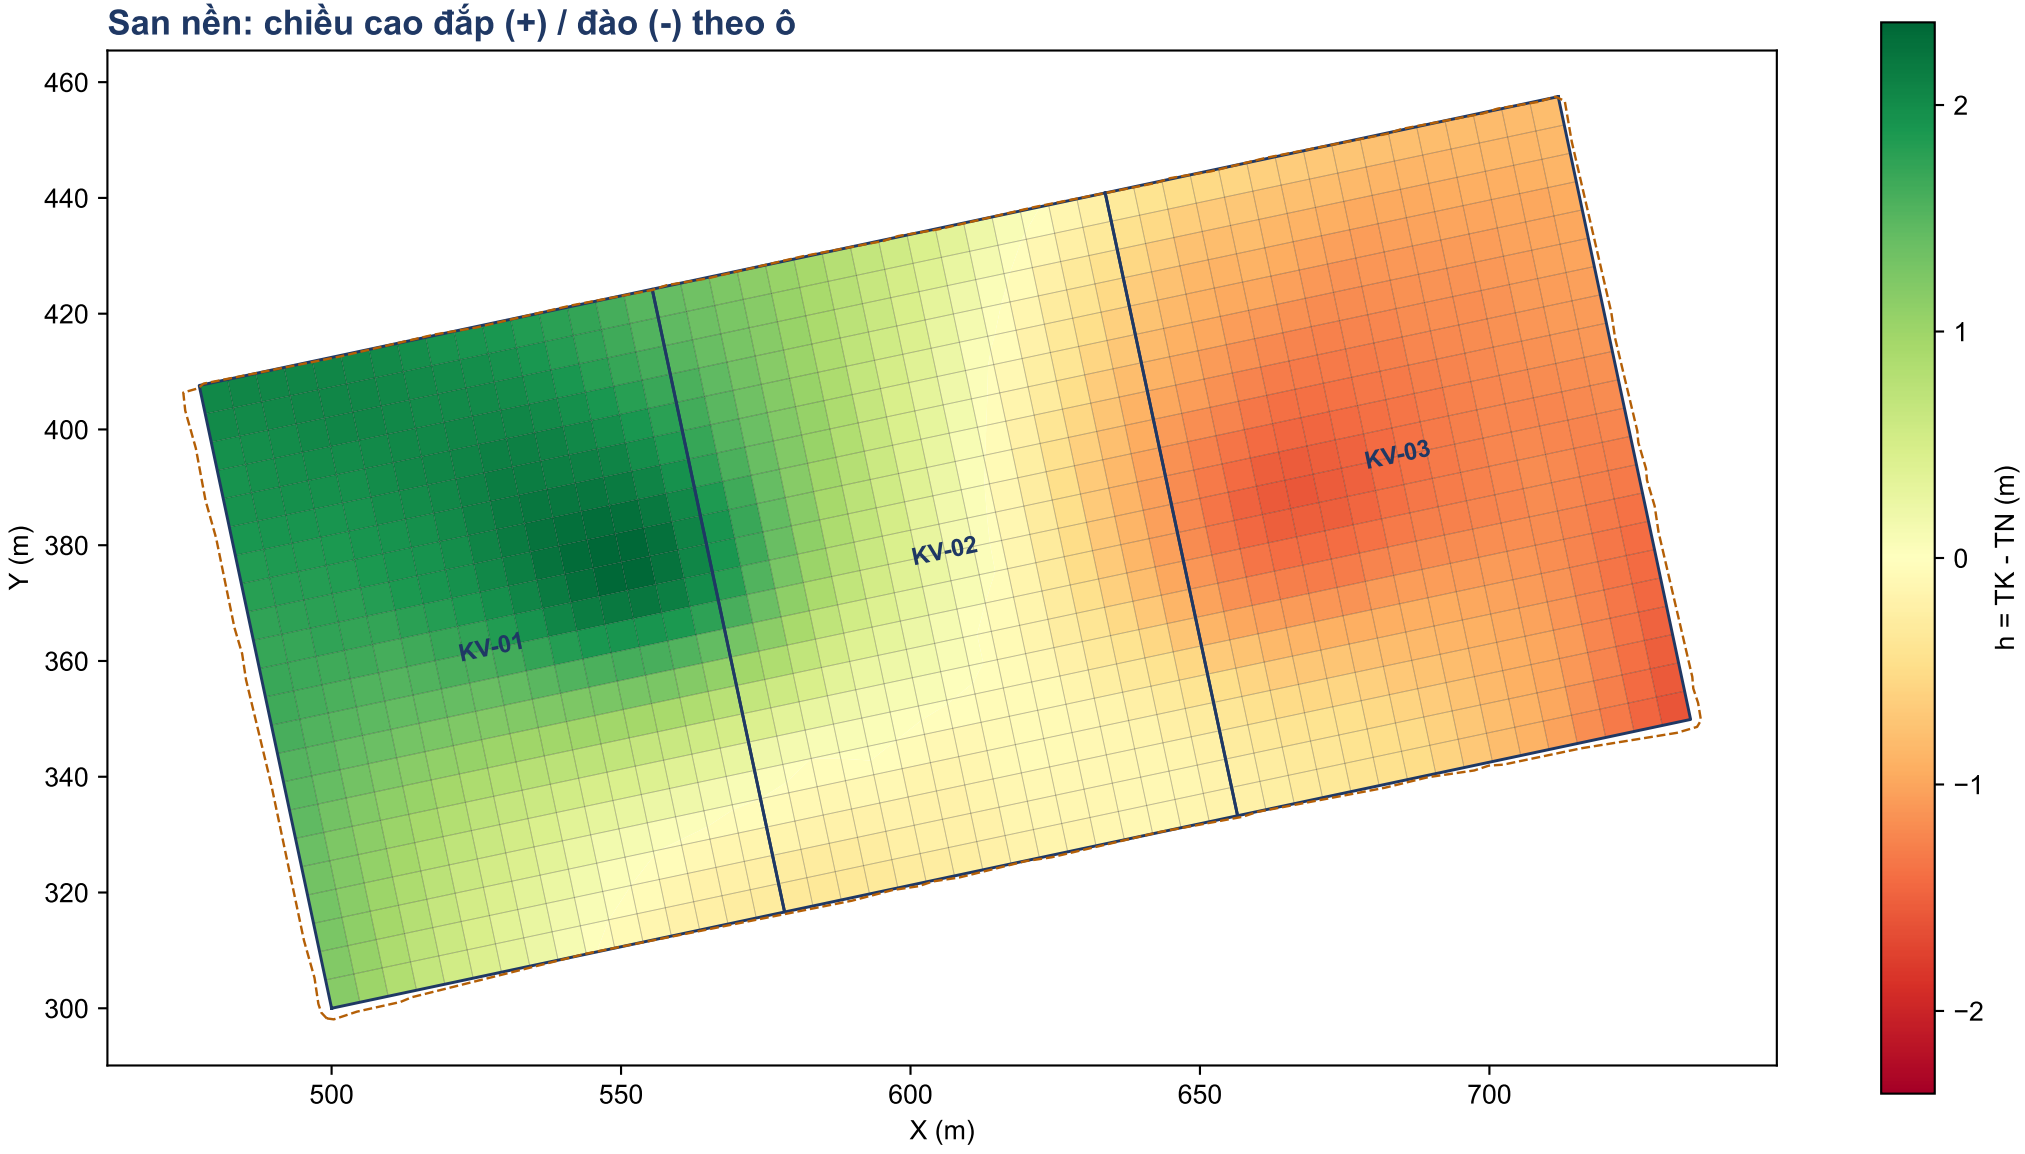
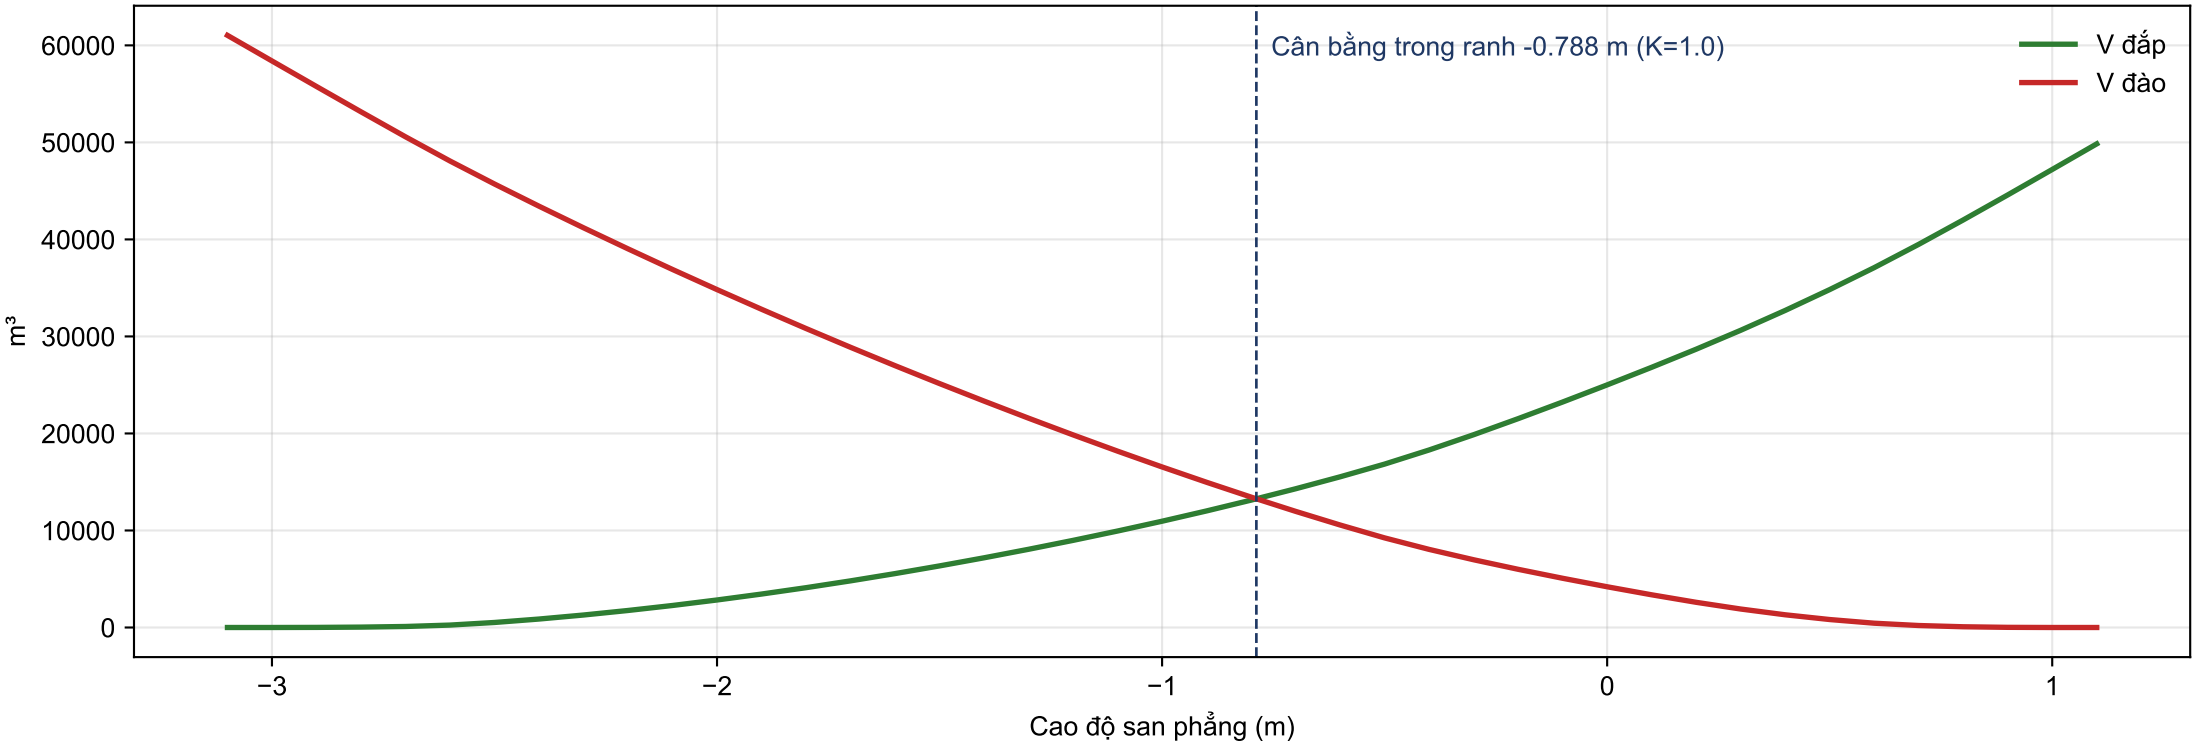

San nền: chiều cao đắp (+) / đào (-) theo ô
KV-01
KV-02
KV-03
Y (m)
X (m)
460
440
420
400
380
360
340
320
300
500
550
600
650
700
h = TK - TN (m)
2
1
0
−1
−2

Tổng hợp khối lượng (m³)

Khu vực	Cao độ TK	Diện tích (m²)	V đắp ô	V đào ô	V đắp TIN	V đào TIN
KV-01	-0.600	8,800.0	12,411.6	64.7	12,419.9	66.7
KV-02	-0.600	8,800.0	3,110.3	1,327.1	3,111.5	1,331.8
KV-03	-0.600	8,800.0	0.0	9,159.1	0.0	9,165.1
Taluy		538.0	246.0	123.2	246.0	123.2
Hố móng			0.0	2,412.7	0.0	2,412.7
Cọc			0.0	201.1	0.0	201.1
TỔNG		**26,938.0**	**15,767.9**	**13,287.8**	**15,777.4**	**13,300.5**



Các điểm cần kiểm tra

[CẢNH BÁO] KV-01: 25 ô có tâm cách điểm đo gần nhất trên 7.5 m: A-7, A-13, C-2, C-3, D-2, D-3, D-14, D-15, D-19, E-19, E-20, I-22
[CẢNH BÁO] KV-02: 19 ô có tâm cách điểm đo gần nhất trên 7.5 m: A-7, B-4, E-7, F-8, H-1, H-14, H-15, H-16, I-1, I-7, J-7, K-2
[CẢNH BÁO] KV-03: 22 ô có tâm cách điểm đo gần nhất trên 7.5 m: A-7, B-7, C-2, C-7, C-8, C-9, C-22, J-8, K-8, K-14, K-15, K-20