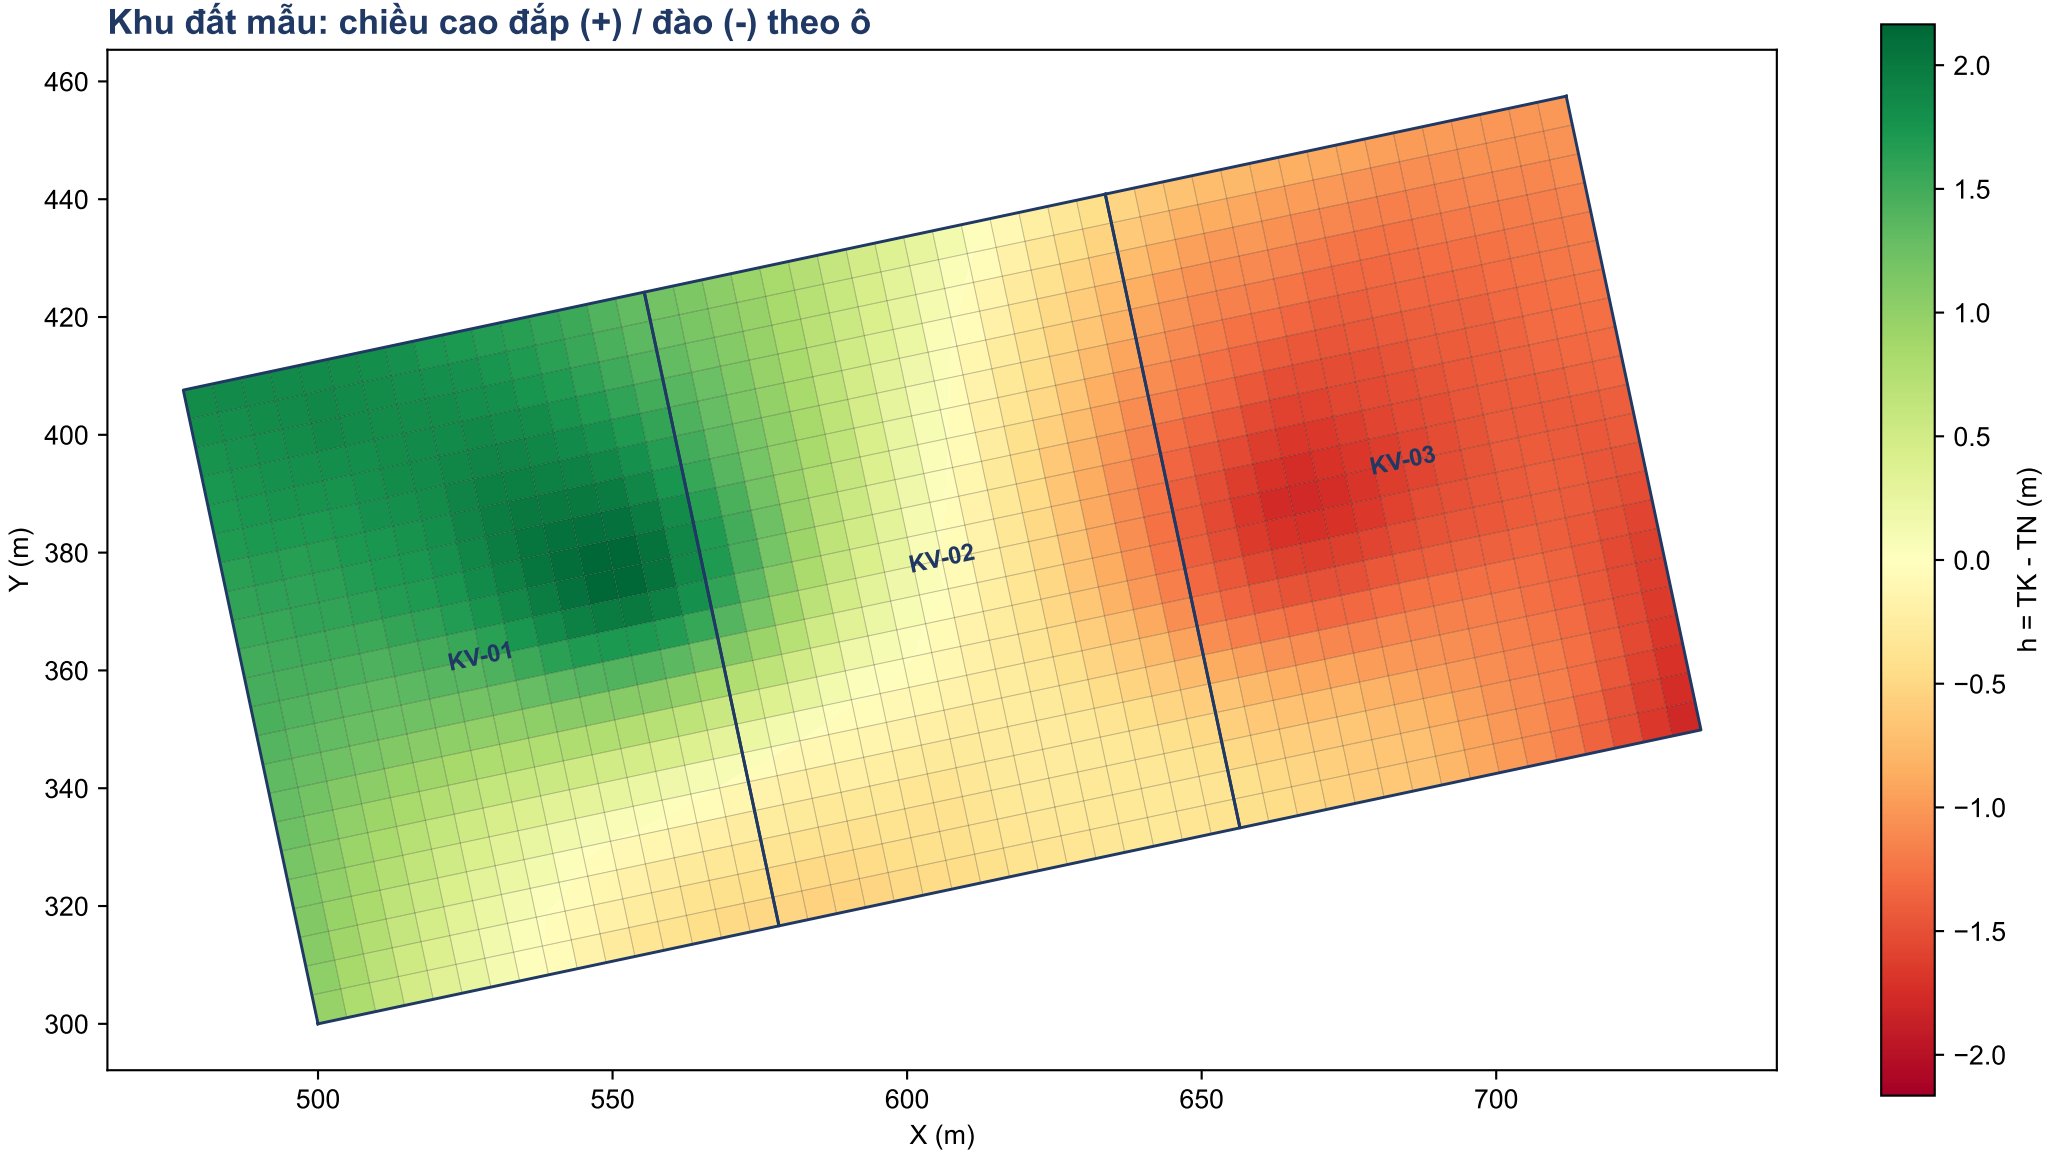
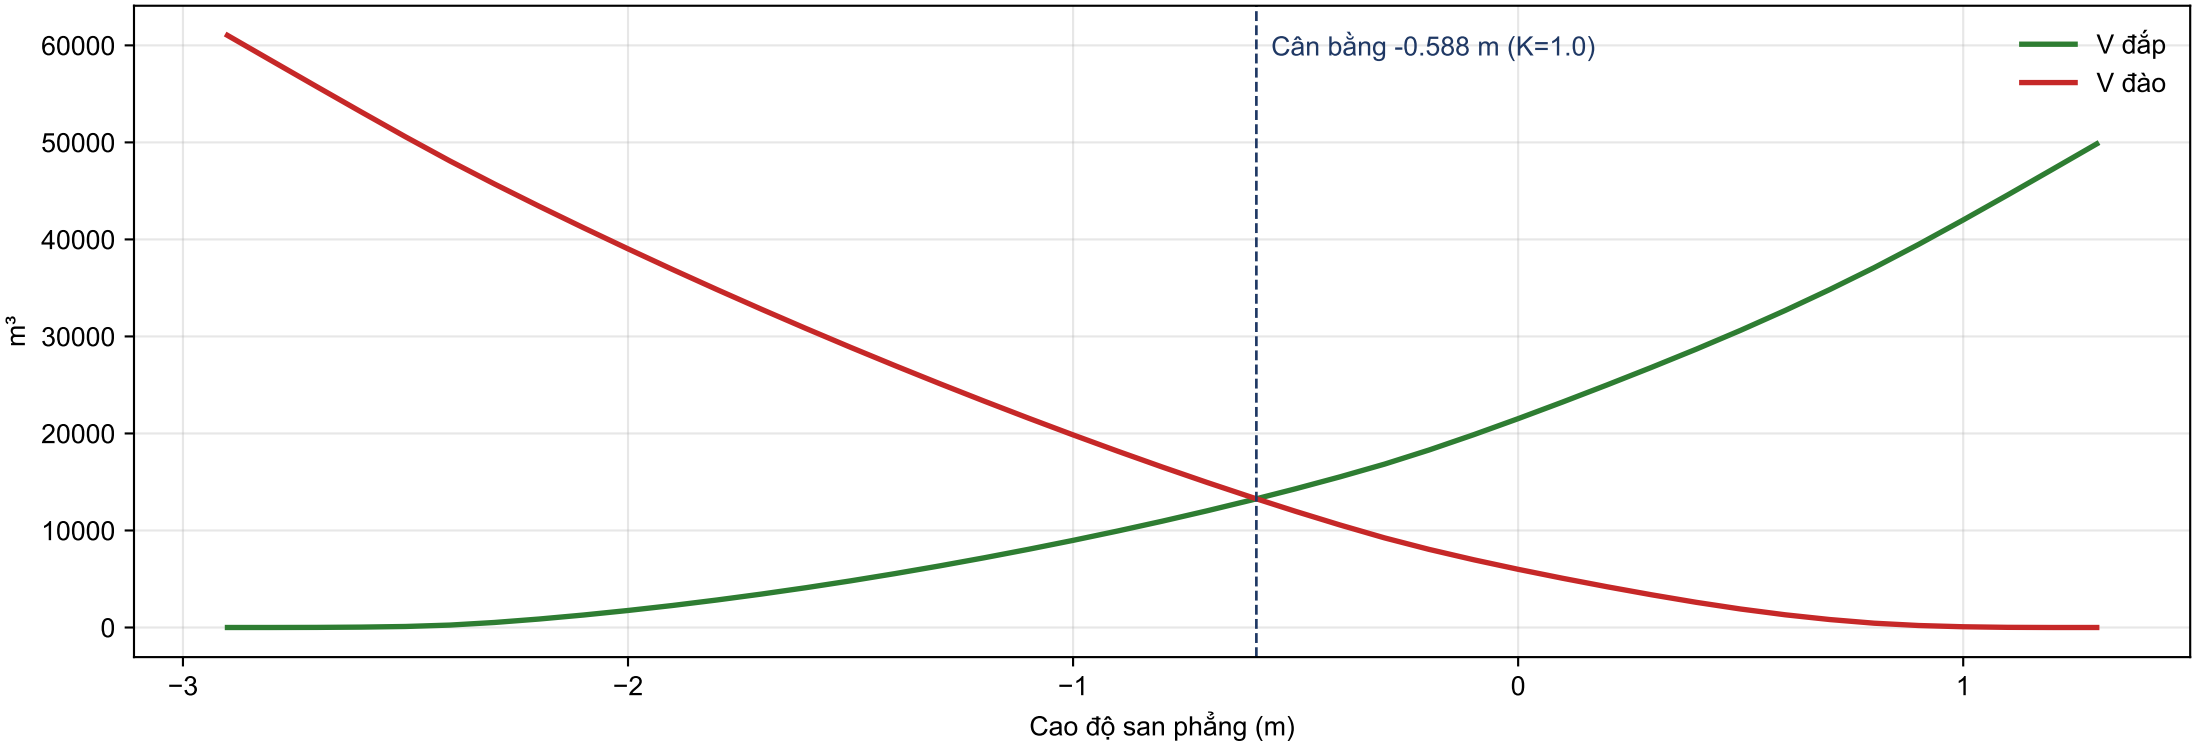

Khu đất mẫu: chiều cao đắp (+) / đào (-) theo ô
KV-01
KV-02
KV-03
Y (m)
X (m)
460
440
420
400
380
360
340
320
300
500
550
600
650
700
h = TK - TN (m)
2.0
1.5
1.0
0.5
0.0
−0.5
−1.0
−1.5
−2.0

Tổng hợp khối lượng (m³)

Khu vực	Cao độ TK	Diện tích (m²)	V đắp ô	V đào ô	V đắp TIN	V đào TIN
KV-01	-0.600	8,800.0	10,775.7	188.7	10,785.3	192.1
KV-02	-0.600	8,800.0	2,340.8	2,317.1	2,343.1	2,323.4
KV-03	-0.600	8,800.0	0.0	10,919.1	0.0	10,925.1
TỔNG		**26,400.0**	**13,116.5**	**13,424.9**	**13,128.4**	**13,440.6**



Các điểm cần kiểm tra

[CẢNH BÁO] KV-01: 25 ô có tâm cách điểm đo gần nhất trên 7.5 m: A-7, A-13, C-2, C-3, D-2, D-3, D-14, D-15, D-19, E-19, E-20, I-22
[CẢNH BÁO] KV-02: 19 ô có tâm cách điểm đo gần nhất trên 7.5 m: A-7, B-4, E-7, F-8, H-1, H-14, H-15, H-16, I-1, I-7, J-7, K-2
[CẢNH BÁO] KV-03: 22 ô có tâm cách điểm đo gần nhất trên 7.5 m: A-7, B-7, C-2, C-7, C-8, C-9, C-22, J-8, K-8, K-14, K-15, K-20